


¼ Mile
Sheet

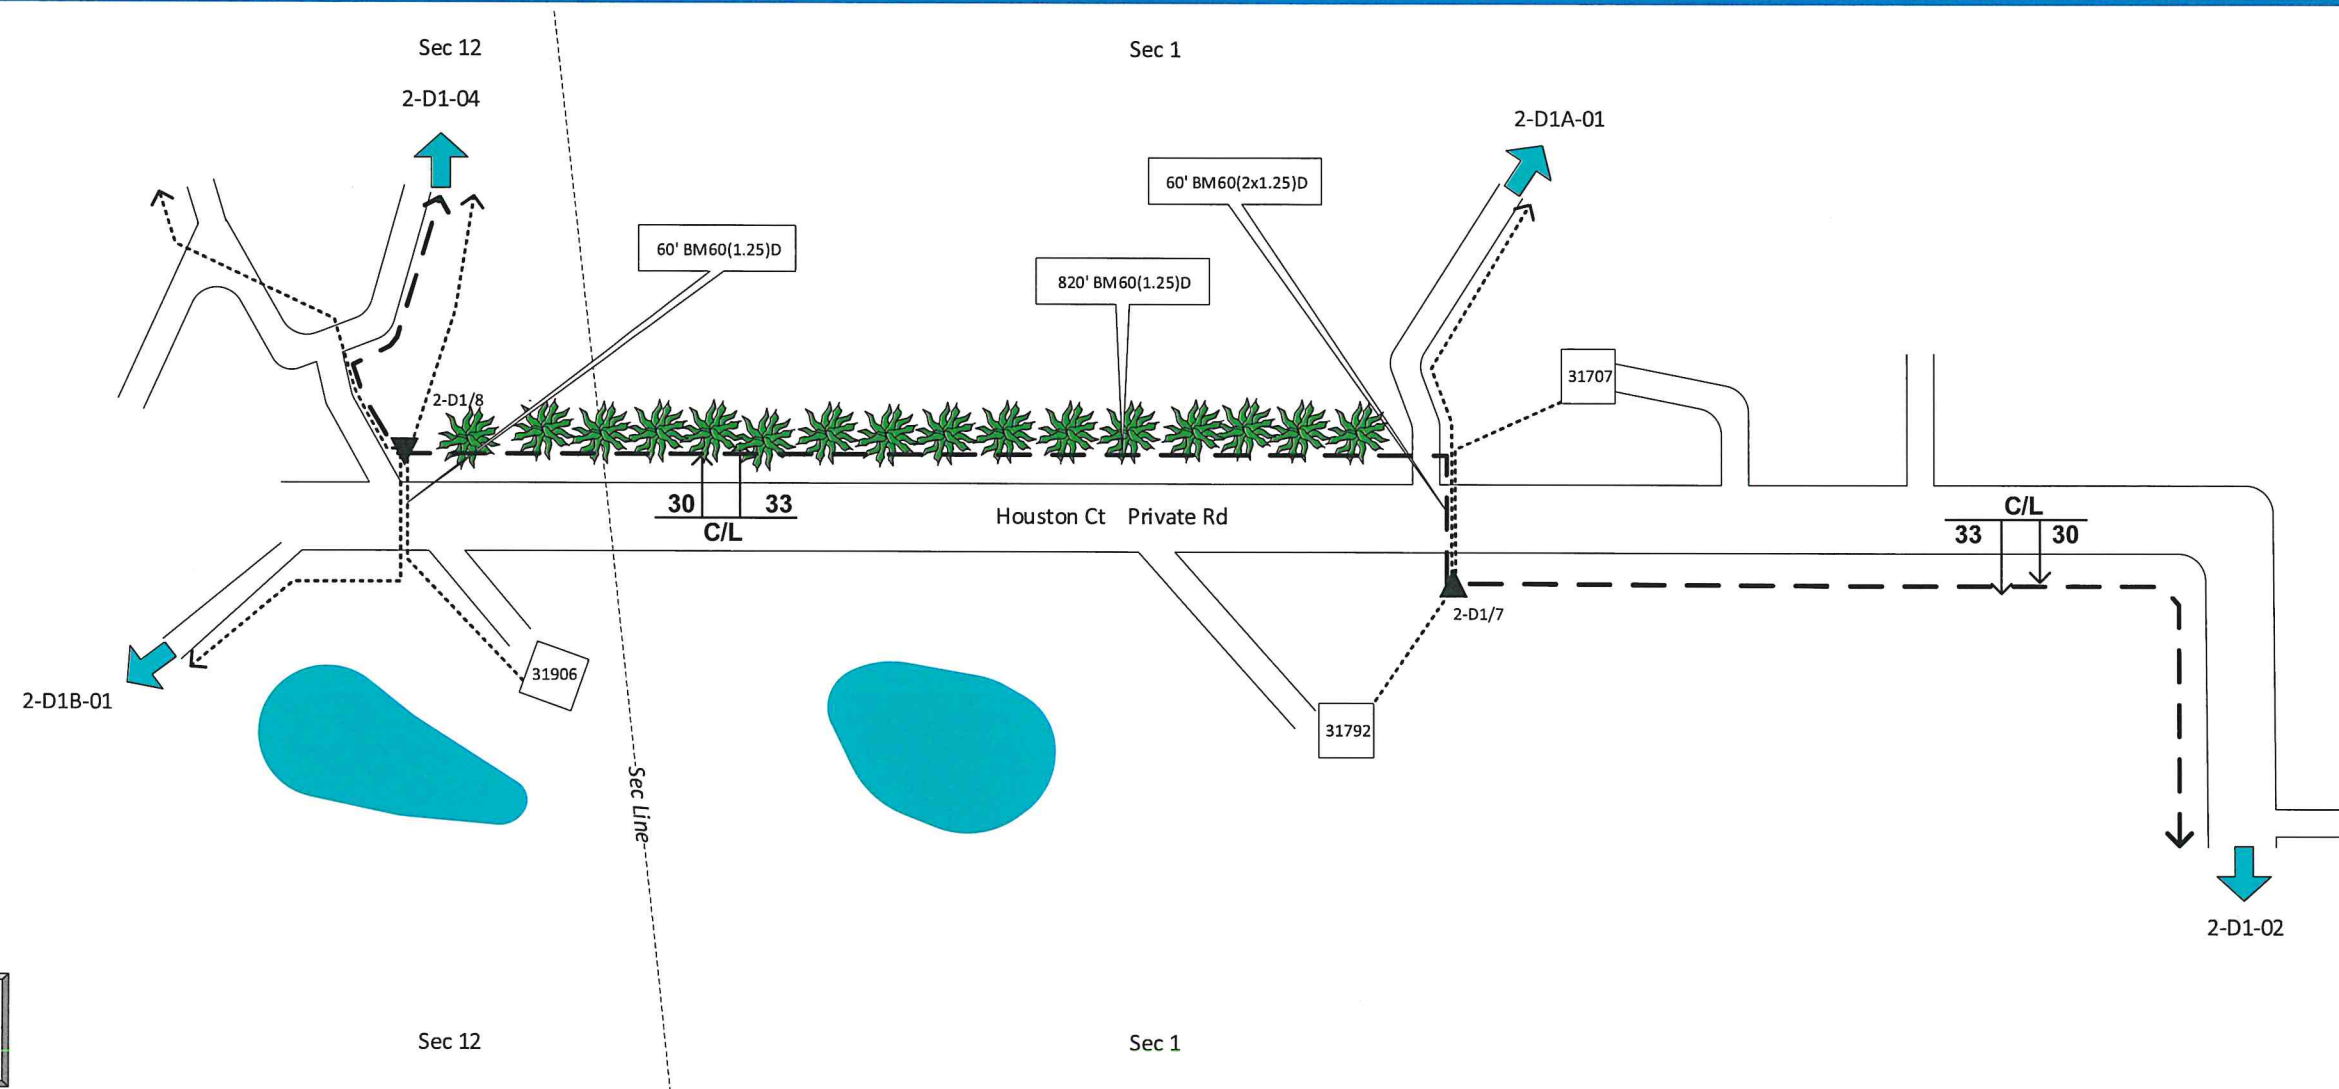

Contractor to place drops
with mainline in ROW.

From	To	PType	Units	Feet	BM		HO		ONT	Remarks
(2-D1/6)	2-D1/7	BDO4	BFO 48W	1170	2(5/8)(8)	1	1	1		
	2-D1/7						1	2		
2-D1/7	31707 Houston Ct		SEBO 4	184	60(2x1.25)D	60			HS	
	31707 Houston Ct				83	1				
2-D1/7	31792 Houston Ct		SEBO 4	256	83	1			HS	
2-D1/7	2-D1/8	BDO4	BFO 48W	918	2(5/8)(8)	1	1	1		
	2-D1/8				60(1.25)D	820	1	3		
2-D1/8	31906 Houston Ct		SEBO 4	242	60(1.25)D	60			HS	
	31906 Houston Ct				83	1				

As Staked: Panora Fiber

Name: 2-D1-03

WO: VPS_REDFIELD_23

Exch: Redfield

County: Dallas


State: JA ROW: Private

TWSP: 78N RNG: 29W SECT: 1

Route: 2-D1

Fielded By: TRU/SH Date: 3/23

Revised By: TL Date: 10-24


VantagePoint

Drawing Not to Scale

Sheet	3	of	4
-------	---	----	---

Sec 12

[illegible]

As Staked:		Panora Fiber	
Name:		2-D1-04	
WO:		VPS_REDFIELD_23	
Exch:		Redfield	
County:		Dallas	
State:		IA	ROW: <u>Private</u>
TWSP:		<u>78N</u>	RNG: <u>29W</u> SECT: <u>12</u>
Route:		2-D1	
Fielded By:		<u>TRL/SH</u>	Date: <u>3/23</u>
Revised By:		<u>TL</u>	Date: <u>10-24</u>
 VantagePoint			
<i>Drawing Not to Scale</i>			
Sheet	4	of	4

Sec 12

[illegible]

As Staked: Panora Fiber

Name: 2-D1B-01

WO: VPS_REDFIELD_23

Exch: Redfield

County: Dallas


State: IA ROW: Public

TWSP: 78N RNG: 29W SECT: 12

Route: 2-D1B

Fielded By: TRL/SH Date: 3/23

Revised By: _____ Date: _____

 **VantagePoint**

Drawing Not to Scale

Sheet	1	of	1
-------	---	----	---